



PLANTA CON REFERENCIA DE MOBILIARIO

M01: alacenas + mueble bajomesada.
M02: barra móvil
M03: mueble baño

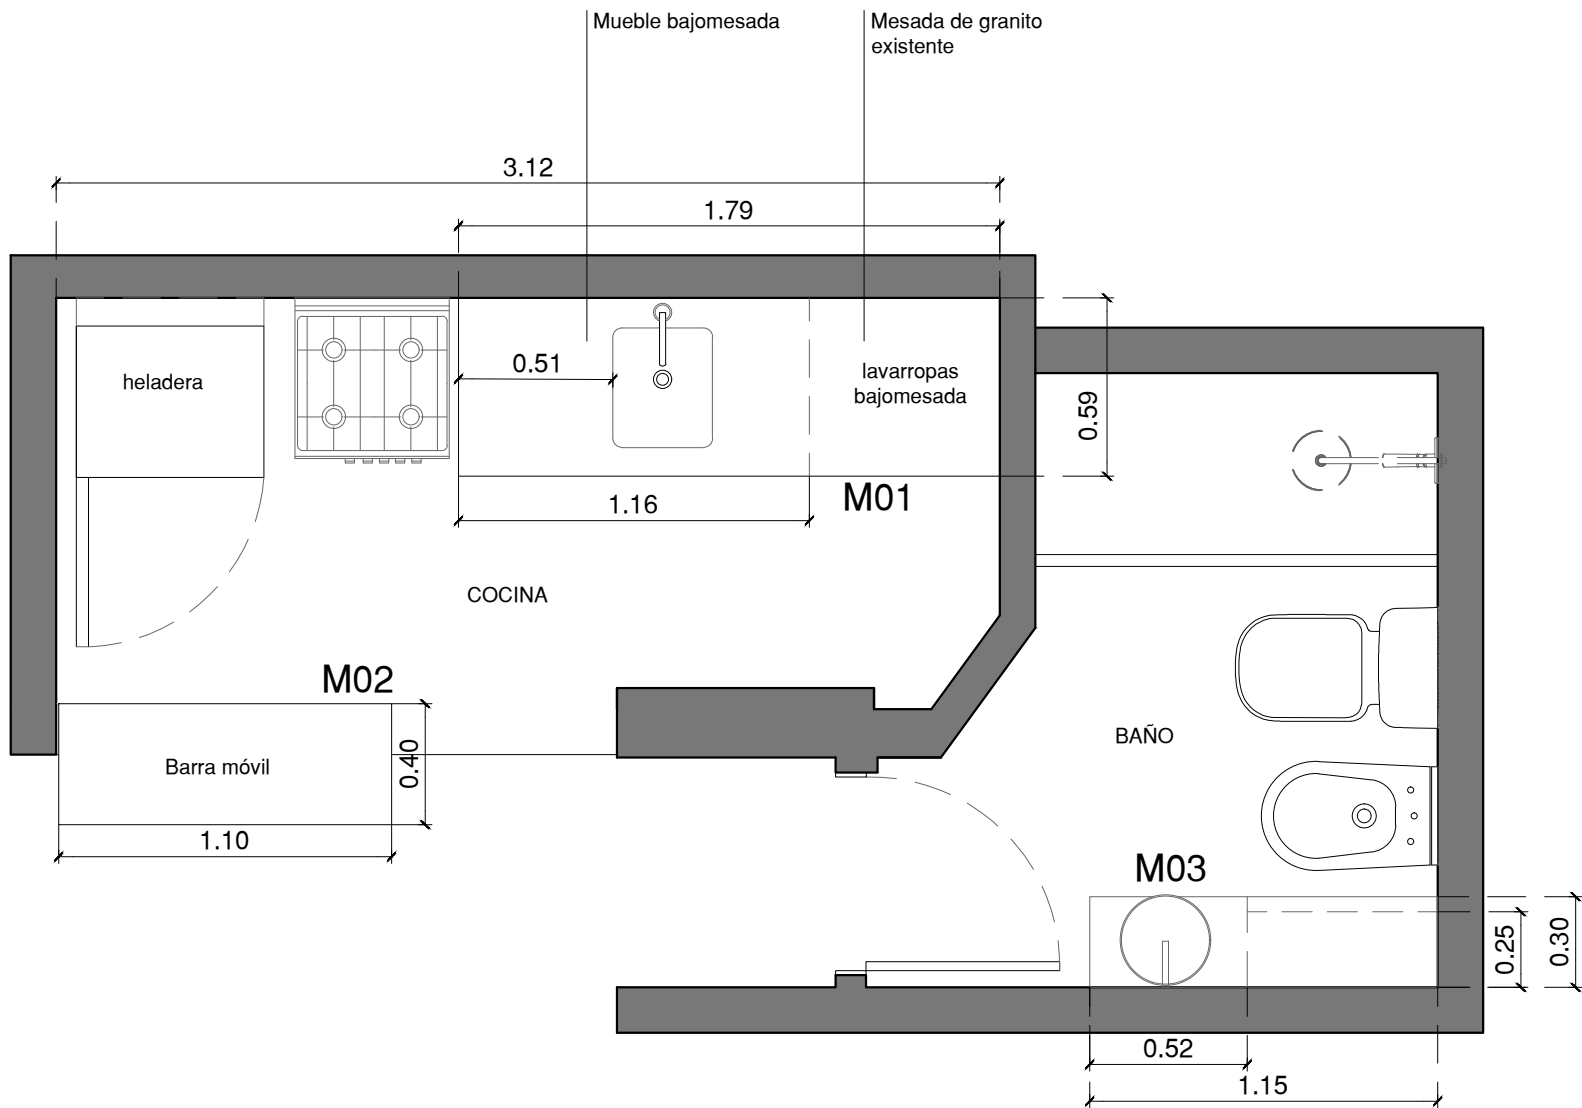

Ciente / Proyecto:	Contenido plano:	N°Plano	Escala	
Remodelación D.Quirós	PLANTA GENERAL	01	1:25	Archivo: DQUIROS_Mobiliario.dwg
		Rubro:	MOBILIARIO	Fecha: 05-05-2025

Mueble bajomesada con cajonera y puertas con estante en melamina MDF terminación gris Ceniza
Alacenas en melamina MDF terminación gris Ceniza con nicho para vinos en melamina Cajù

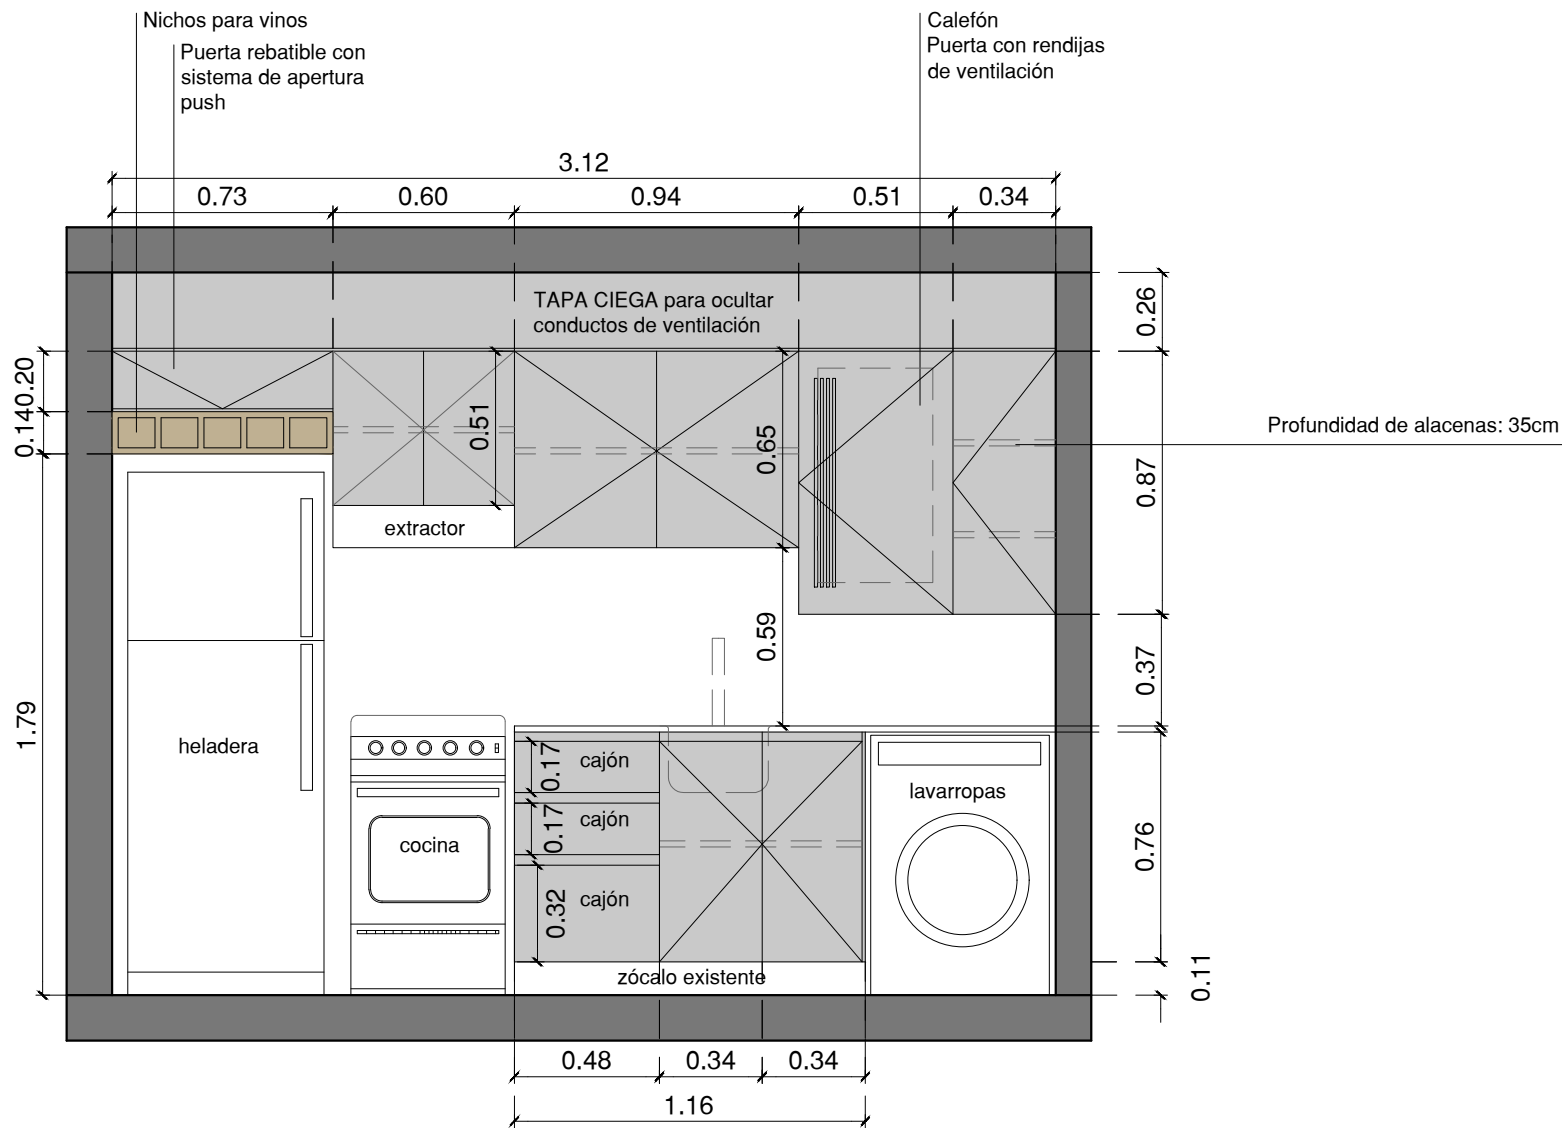

Cliente / Proyecto:

Remodelación D.Quirós

Contenido plano:

VISTA COCINA

N°Plano

02

Rubro:

Escala

1:25


MOBILIARIO

Archivo: DQUIROS_Mobiliario.dwg


Fecha:

05-05-2025


Barra en estructura de caño con tapa superior de melamina Cajú (4cm de espesor)
Caño de 3x3 pintado en tono similar a melamina gris Ceniza

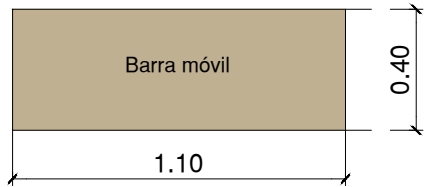

PLANTA

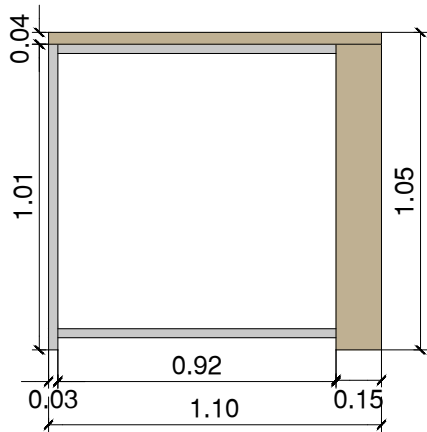

VISTA FRONTAL

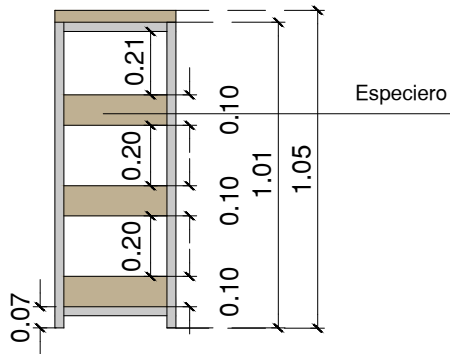

VISTA LATERAL



Cliente / Proyecto:

Remodelación D.Quirós

Contenido plano:

BARRA MÓVIL

N°Plano

03

Rubro:

Escala

1:25


MOBILIARIO

Archivo: DQUIROS_Mobiliario.dwg


Fecha:

05-05-2025

Mueble bajo bacha en baño, con 2 puertas de abrir común, en melamina Cajú y un estante de 25cm de profundidad

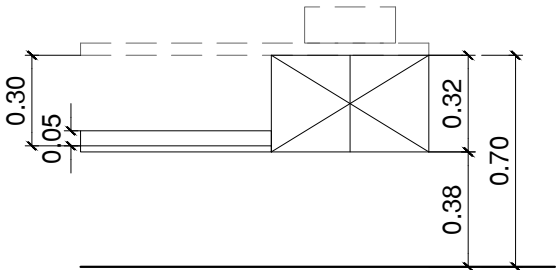

VISTA FRONTAL

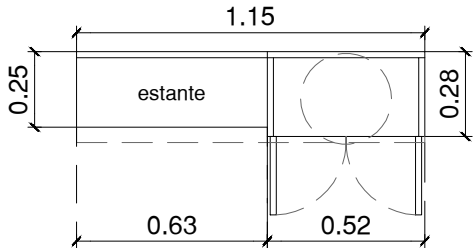

PLANTA



Cliente / Proyecto:

Remodelación D.Quirós

Contenido plano:

MUEBLE VANITORY

NºPlano

04

Rubro:

Escala

1:25

MOBILIARIO

Archivo: DQUIROS_Mobiliario.dwg

Fecha:

05-05-2025